



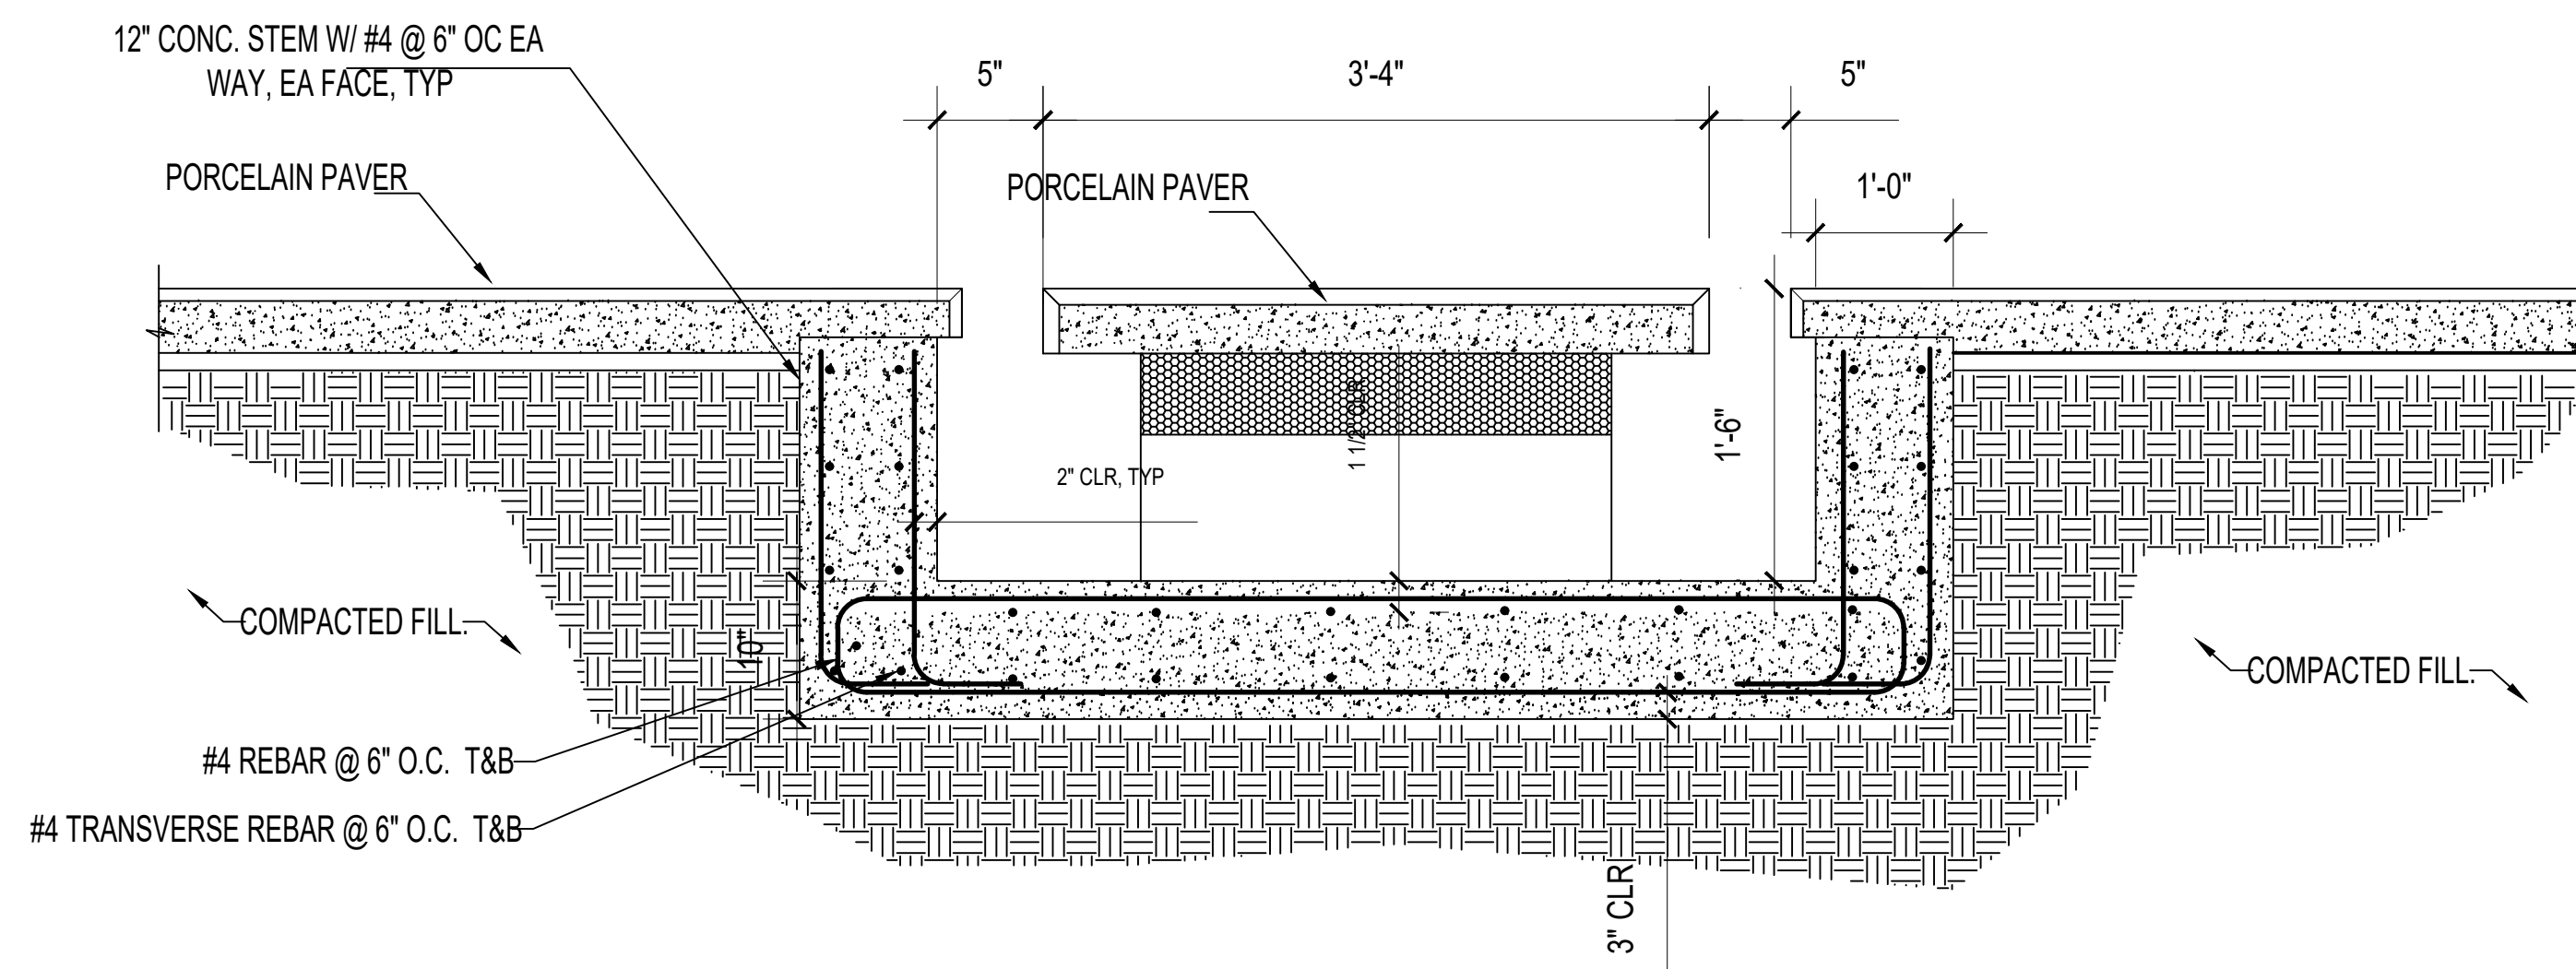


01	DETAIL
----	--------

SCALE: NTS

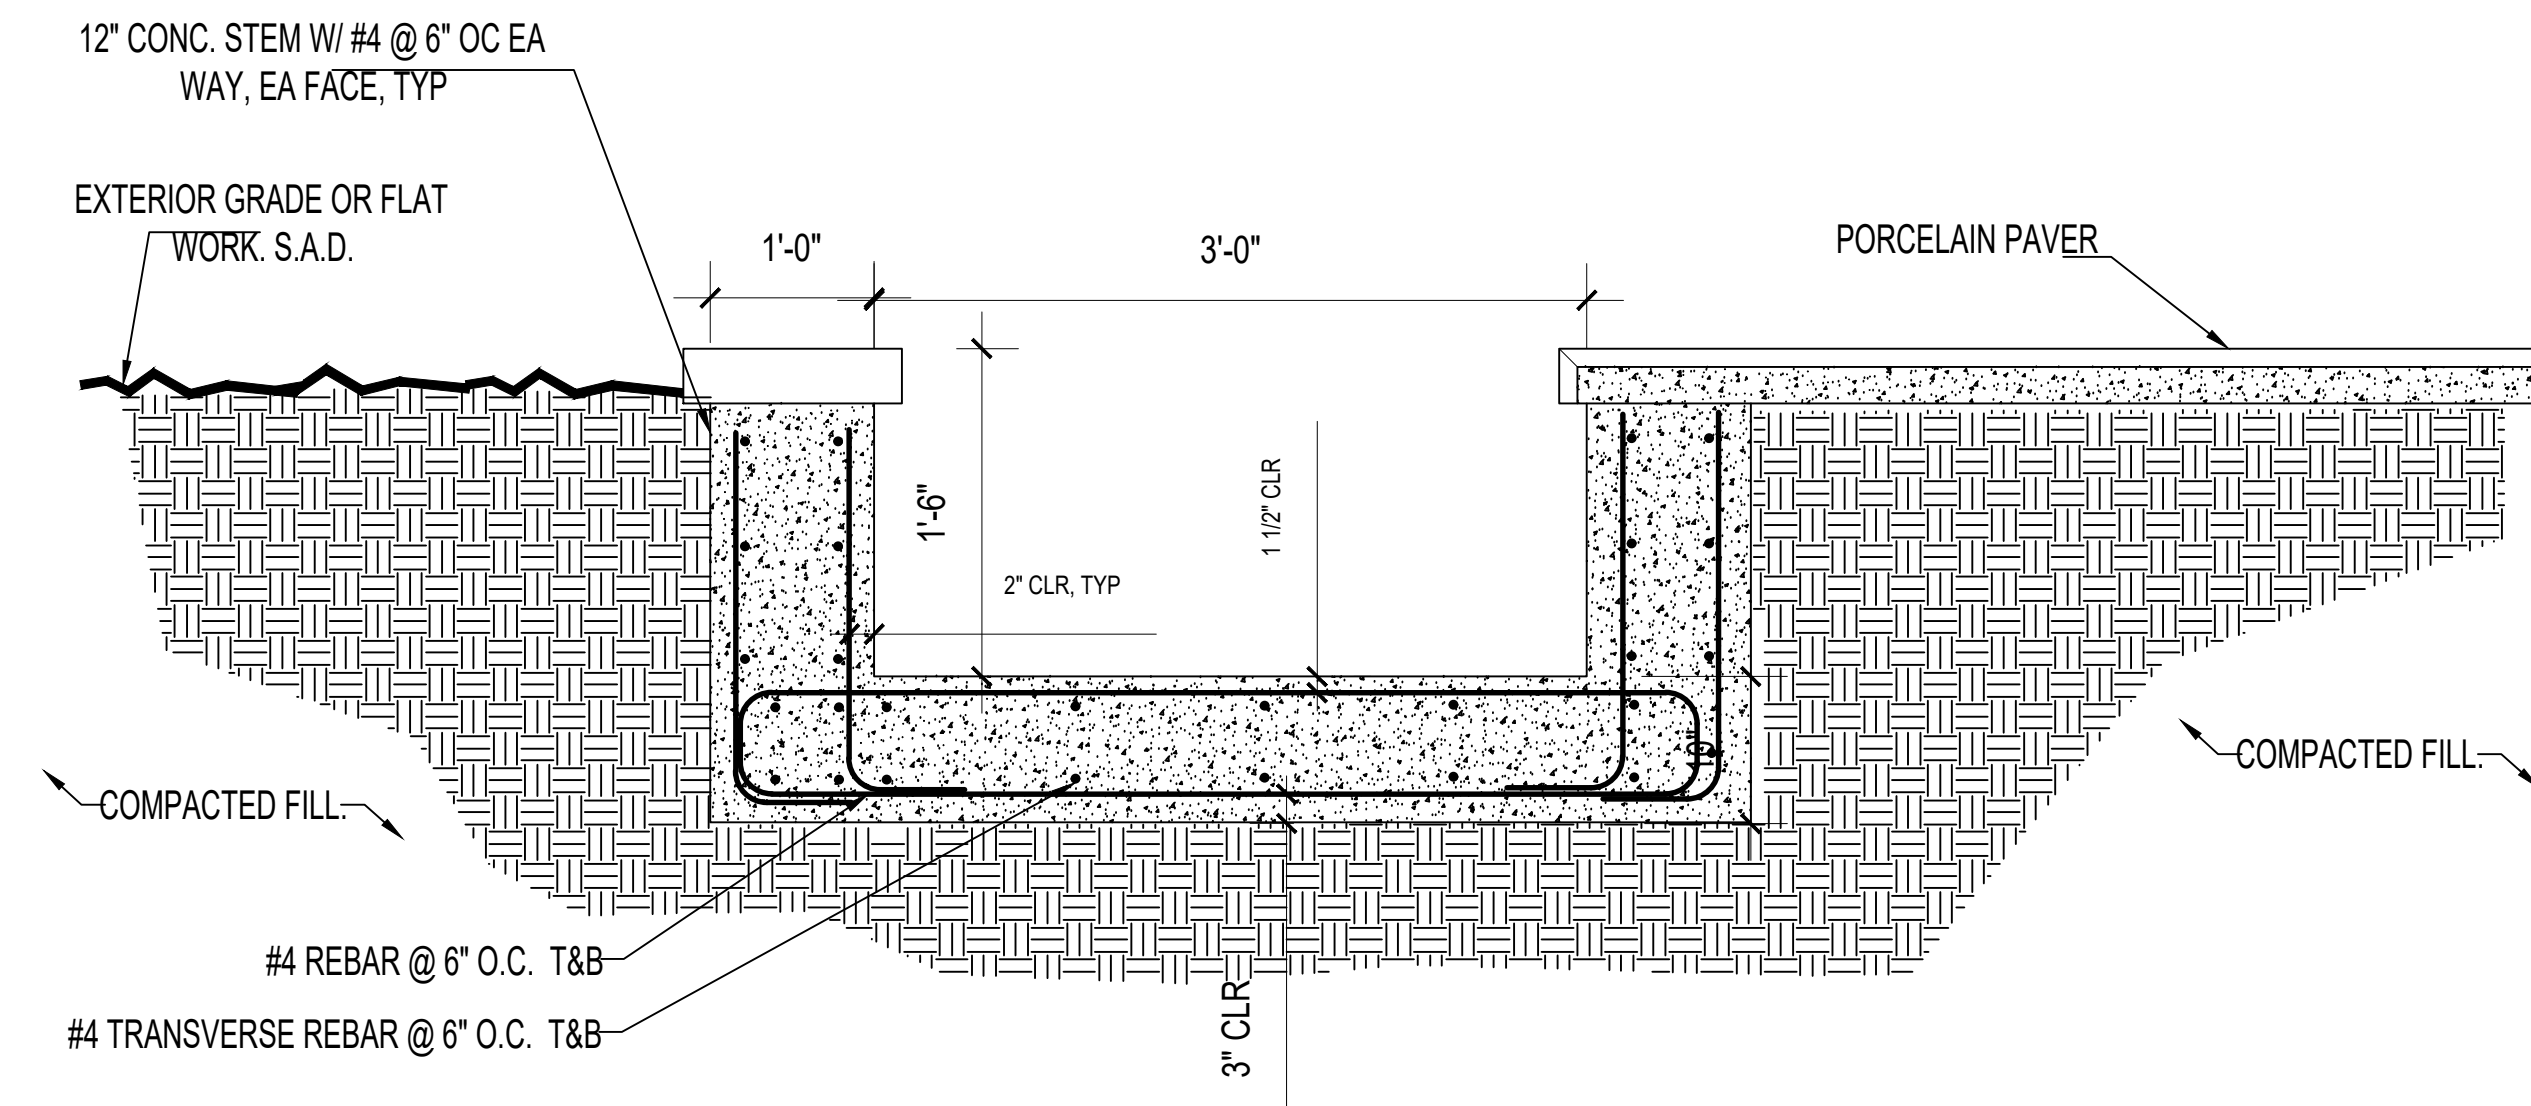


s	02	DETAIL
---	----	--------

SCALE: NTS

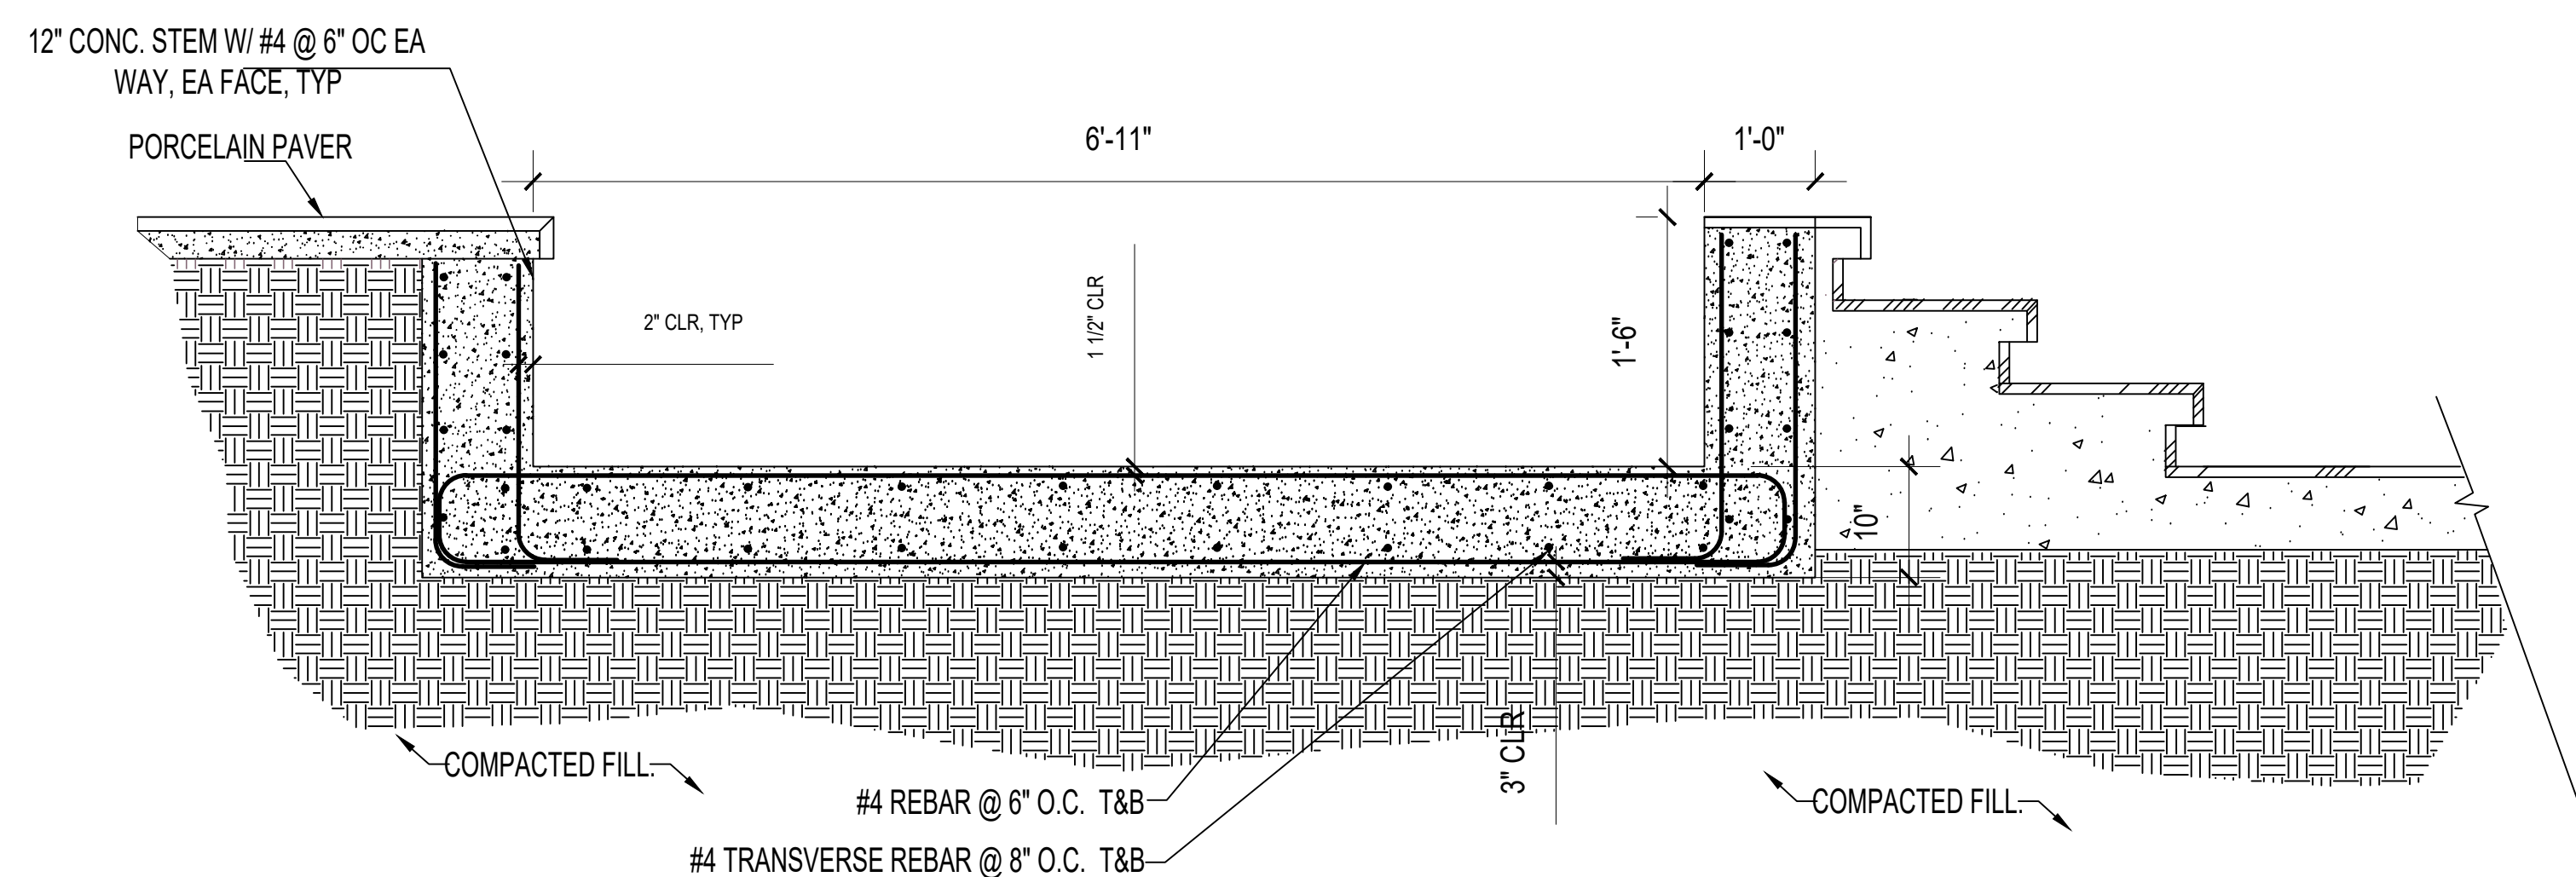

03	DETAIL
----	--------

SCALE: NTS

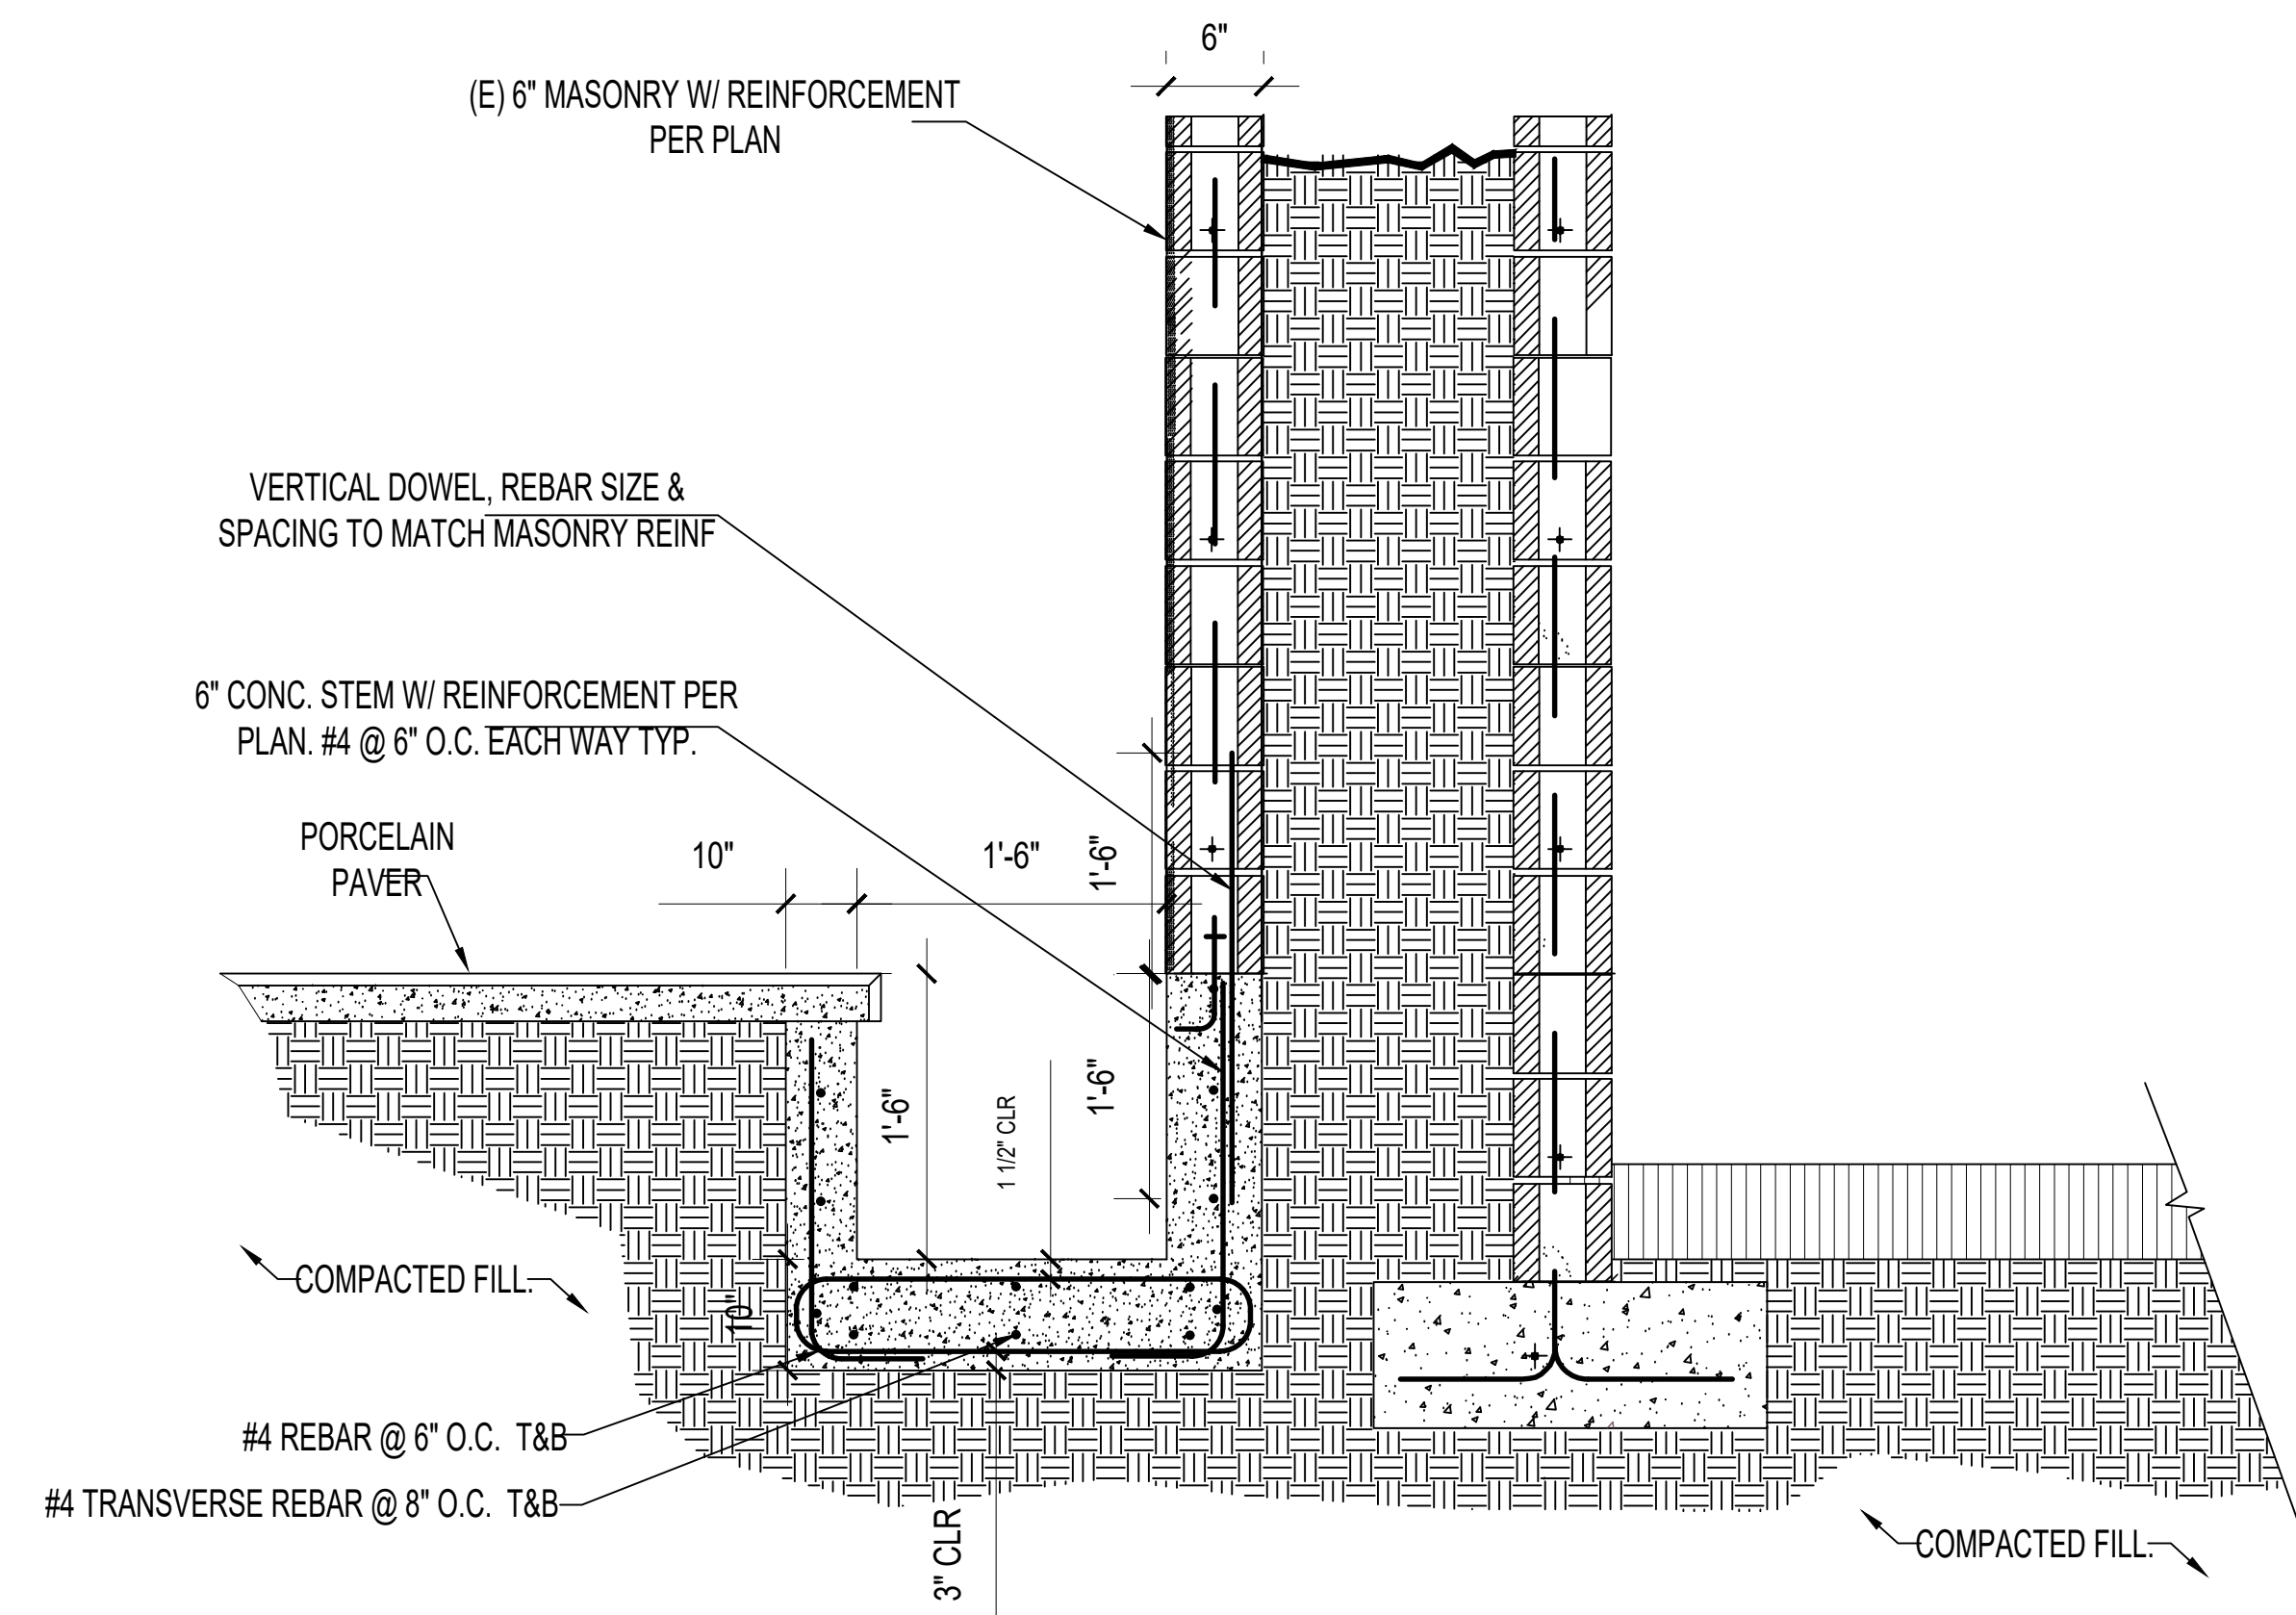

s	04	DETAIL
---	----	--------

SCALE: NTS



1401 Doug Baker Boulevard
Birmingham, AL 35242
Tel: +1 659-307-9885
Email: info@evervastco.com

Proposed Kinnett Residence
Lot 29, 78293 Birkdale Court
La Quinta, CA 92253

PROJECT TITLE:

PROFESSIONAL SEAL:

[illegible]

DRAWING TITLE:

TYPICAL DETAILS

S2.2